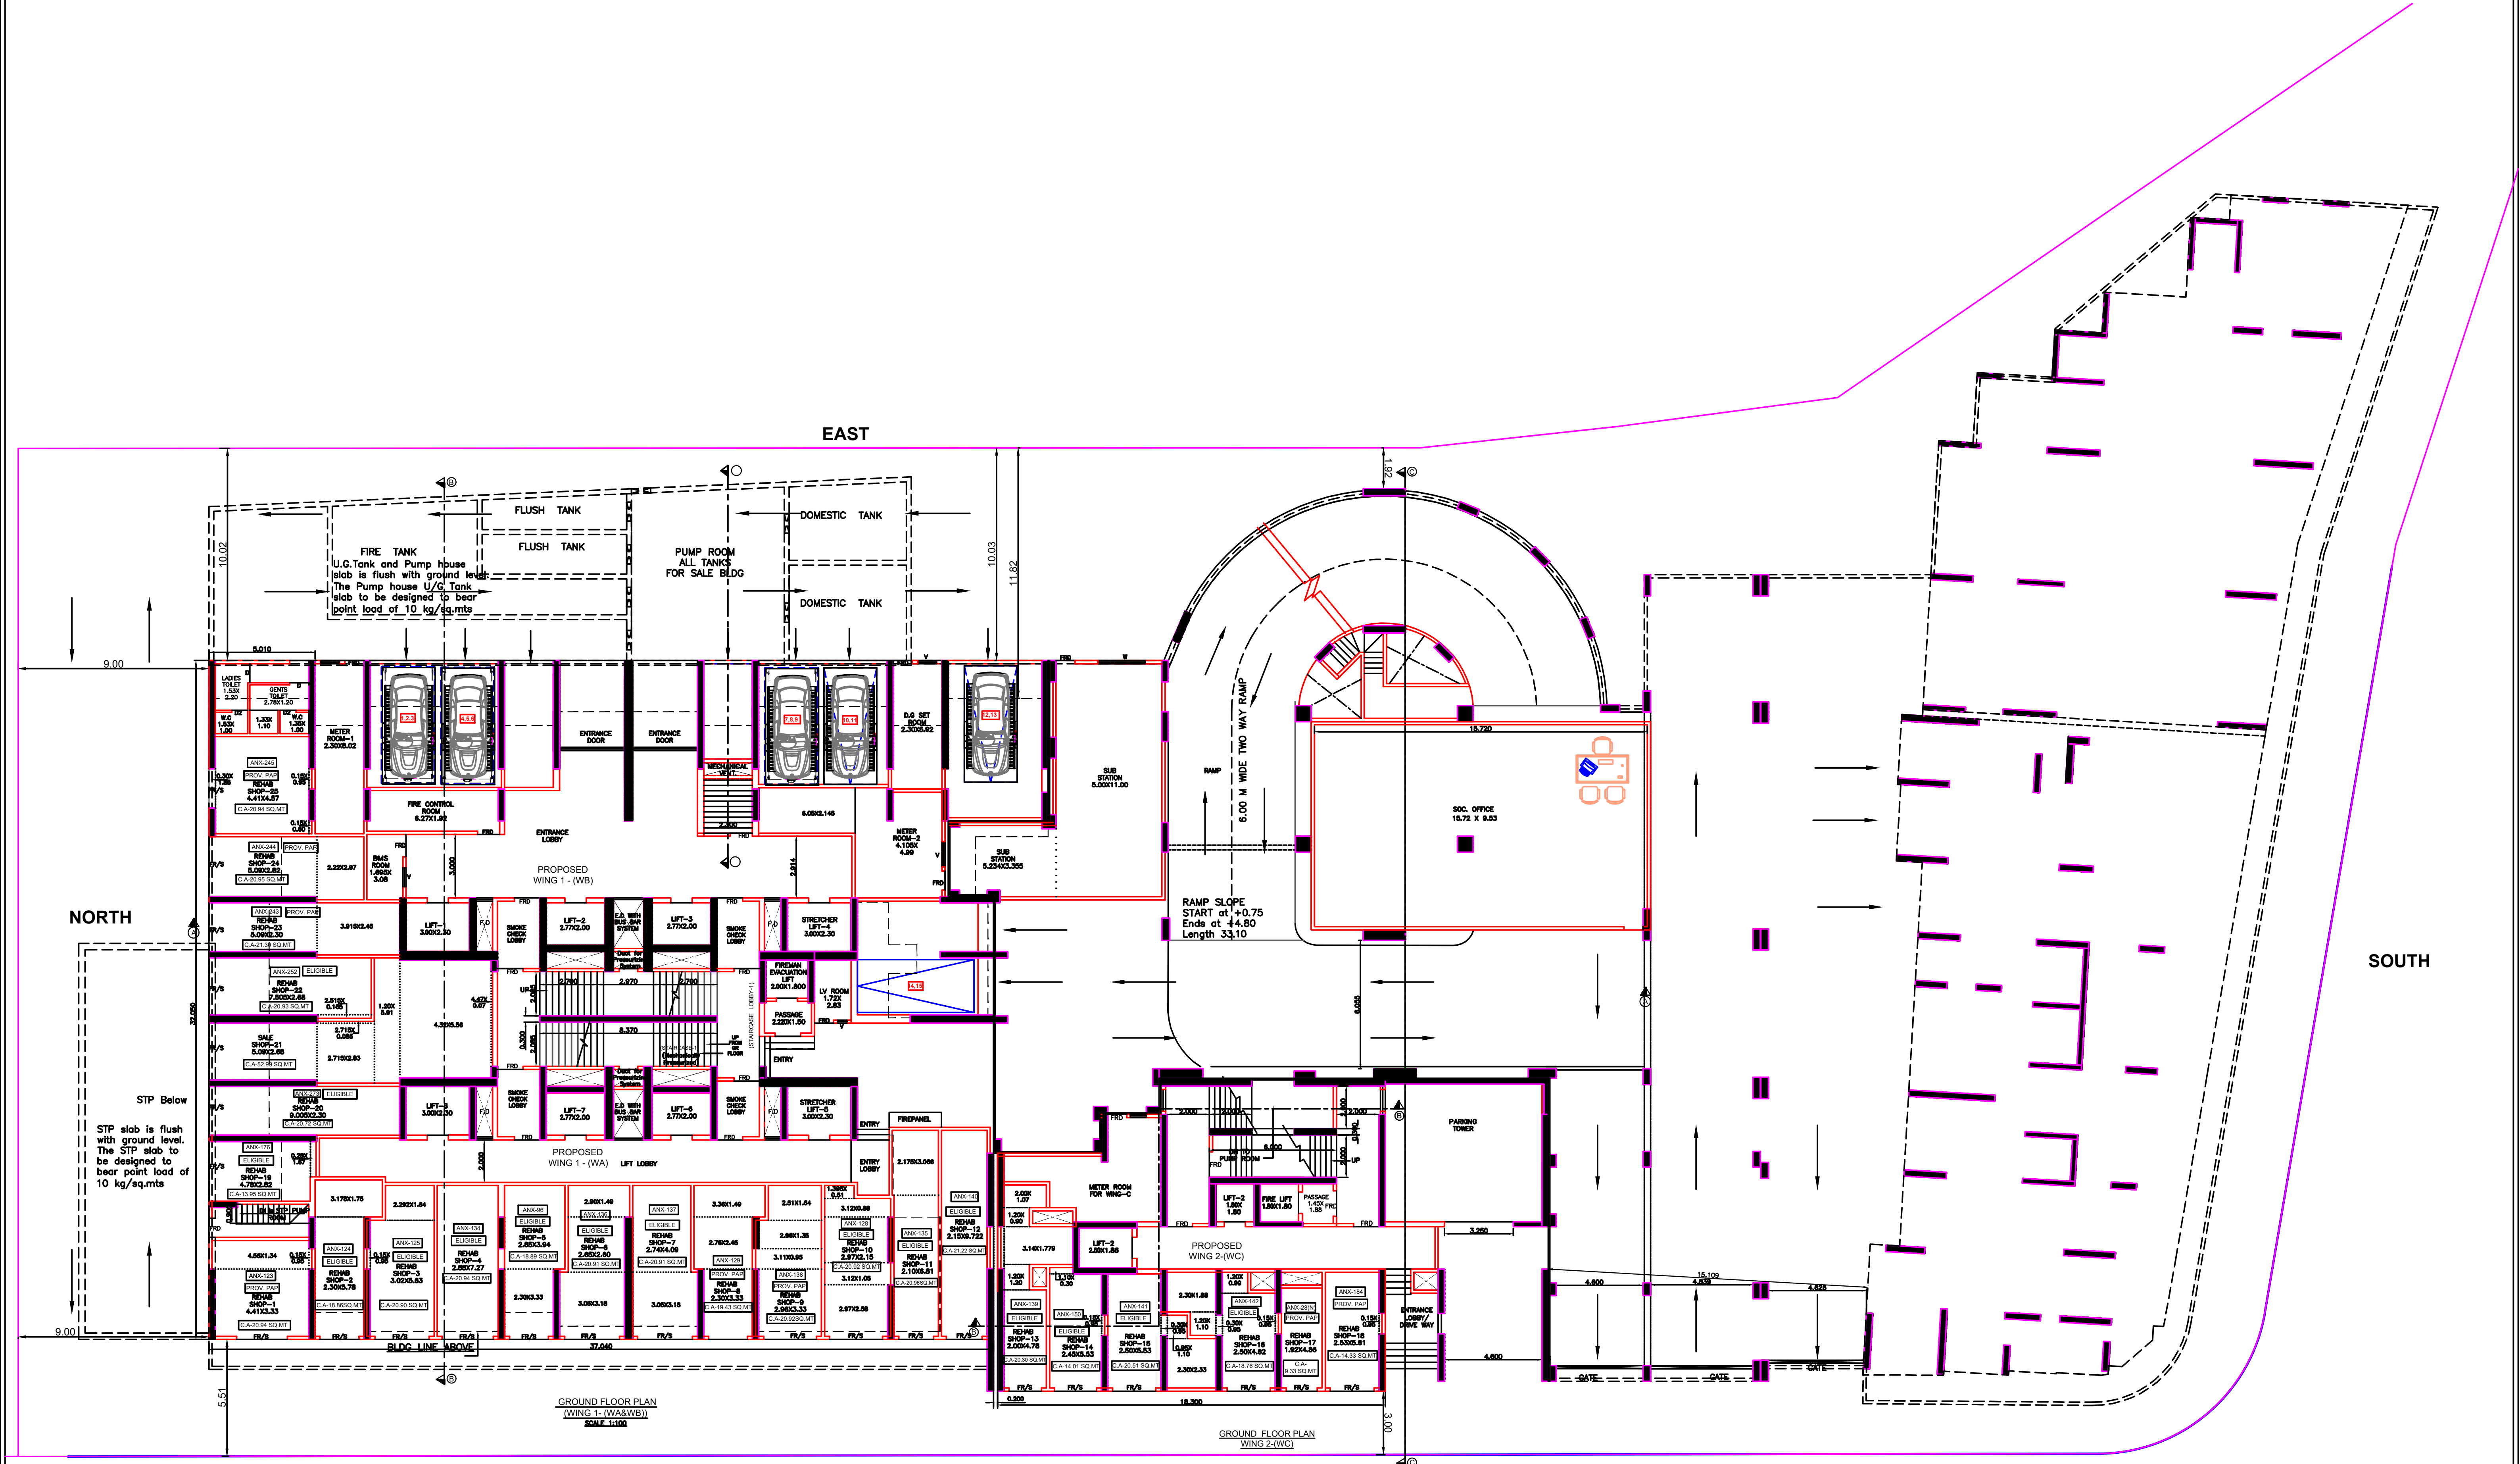
EAST
NORTH
SOUTH
FLUSH TANK
FLUSH TANK
FIRE TANK
U.G.Tank and Pump house slab is flush with ground level. The Pump house U/G Tank slab to be designed to bear point load of 10 kg/sq.mts
PUMP ROOM
ALL TANKS
FOR SALE BLDG
DOMESTIC TANK
DOMESTIC TANK
10.02
10.03
11.82
1.92
9.00
5.010
LADIES TOILET 1.53X 2.20
GENTS TOILET 2.78X1.20
W.C 1.53X 1.00
1.33X 1.10
W.C 1.35X 1.00
METER ROOM-1 2.30X8.02
1,2,3
4,5,6
7,8,9
10,11
12,13
14,15
ENTRANCE DOOR
ENTRANCE DOOR
MECHANICAL VENT.
D.G SET ROOM 2.30X5.92
SUB STATION 5.00X11.00
ANX-245
PROV. PAP
REHAB SHOP-25 4.41X4.57
C.A-20.94 SQ.MT
FIRE CONTROL ROOM 6.27X1.92
ENTRANCE LOBBY
6.05X2.145
METER ROOM-2 4.105X 4.99
SUB STATION 5.234X3.355
ANX-244
PROV. PAP
REHAB SHOP-24 5.09X2.82
C.A-20.95 SQ.MT
2.22X2.97
BMS ROOM 1.695X 3.08
PROPOSED WING 1 - (WB)
ANX-243
PROV. PAP
REHAB SHOP-23 5.09X2.30
C.A-21.30 SQ.MT
3.915X2.45
LIFT-1 3.00X2.30
SMOKE CHECK LOBBY
LIFT-2 2.77X2.00
E.D WITH BUS BAR SYSTEM
LIFT-3 2.77X2.00
STRETCHER LIFT-4 3.00X2.30
FIREMAN EVACUATION LIFT 2.00X1.800
LV ROOM 1.72X 2.83
PASSAGE 2.220X1.50
ANX-252
ELIGIBLE
REHAB SHOP-22 7.505X2.88
C.A-20.93 SQ.MT
2.515X 0.165
1.20X 5.91
4.32X5.56
4.47X 0.07
2.700
2.970
2.700
8.370
(STAIRCASE LOBBY-1)
STAIRCASE-1 (Mechanically Pressurized)
UP FROM GR FLOOR
ENTRY
SALE SHOP-21 5.09X2.68
C.A-52.99 SQ.MT
2.715X 0.085
2.715X2.83
32.050
STP Below
STP slab is flush with ground level. The STP slab to be designed to bear point load of 10 kg/sq.mts
ANX-273
ELIGIBLE
REHAB SHOP-20 9.005X2.30
C.A-20.72 SQ.MT
LIFT-8 3.00X2.30
LIFT-7 2.77X2.00
LIFT-6 2.77X2.00
STRETCHER LIFT-5 3.00X2.30
FIREPANEL
ENTRY LOBBY
PROPOSED WING 1 - (WA)
LIFT LOBBY
ANX-176
ELIGIBLE
REHAB SHOP-19 4.78X2.82
C.A-13.95 SQ.MT
UP to STP PUMP ROOM
3.178X1.75
2.292X1.64
2.90X1.49
3.36X1.49
2.51X1.64
2.175X3.066
4.56X1.34
ANX-123
PROV. PAP
REHAB SHOP-1 4.41X3.33
C.A-20.94 SQ.MT
ANX-124
ELIGIBLE
REHAB SHOP-2 2.30X5.78
C.A-18.86SQ.MT
ANX-125
ELIGIBLE
REHAB SHOP-3 3.02X5.63
C.A-20.90 SQ.MT
ANX-134
ELIGIBLE
REHAB SHOP-4 2.88X7.27
C.A-20.94 SQ.MT
ANX-96
ELIGIBLE
REHAB SHOP-5 2.85X3.94
C.A-18.89 SQ.MT
2.30X3.33
ANX-136
ELIGIBLE
REHAB SHOP-6 2.65X2.60
C.A-20.91 SQ.MT
3.05X3.18
ANX-137
ELIGIBLE
REHAB SHOP-7 2.74X4.09
C.A-20.91 SQ.MT
3.05X3.18
2.76X2.45
ANX-129
PROV. PAP
REHAB SHOP-8 2.30X3.33
C.A-19.43 SQ.MT
2.96X1.35
3.11X0.95
ANX-138
PROV. PAP
REHAB SHOP-9 2.96X3.33
C.A-20.92SQ.MT
1.395X 0.61
3.12X0.88
ANX-128
ELIGIBLE
REHAB SHOP-10 2.97X2.15
C.A-20.92 SQ.MT
3.12X1.05
2.97X2.58
ANX-135
ELIGIBLE
REHAB SHOP-11 2.10X6.81
C.A-20.96SQ.MT
ANX-140
ELIGIBLE
REHAB SHOP-12 2.15X9.722
C.A-21.22 SQ.MT
FR/S
BLDG LINE ABOVE
37.040
5.51
RAMP
6.00 M WIDE TWO WAY RAMP
RAMP SLOPE START at +0.75 Ends at +4.80 Length 33.10
15.720
SOC. OFFICE 15.72 X 9.53
6.055
METER ROOM FOR WING-C
2.00X 1.07
1.20X 0.90
3.14X1.779
LIFT-2 2.50X1.86
2.000
UP TO PUMP ROOM
6.000
LIFT-2 1.80X 1.80
FIRE LIFT 1.80X1.80
PASSAGE 1.45X 1.88
PARKING TOWER
PROPOSED WING 2-(WC)
3.250
ANX-139
ELIGIBLE
REHAB SHOP-13 2.00X4.78
C.A-20.30 SQ.MT
ANX-150
ELIGIBLE
REHAB SHOP-14 2.45X5.53
C.A-14.01 SQ.MT
ANX-141
ELIGIBLE
REHAB SHOP-15 2.50X5.53
C.A-20.51 SQ.MT
2.30X1.88
1.20X 1.10
0.95X 1.10
2.30X2.33
ANX-142
ELIGIBLE
REHAB SHOP-16 2.50X4.62
C.A-18.76 SQ.MT
ANX-28(N)
PROV. PAP
REHAB SHOP-17 1.92X4.86
C.A- 9.33 SQ.MT
ANX-184
PROV. PAP
REHAB SHOP-18 2.53X5.61
C.A-14.33 SQ.MT
ENTRANCE LOBBY/ DRIVE WAY
0.200
18.300
3.00
4.600
4.600
15.109
4.839
4.626
GATE
GATE
FRD

GROUND FLOOR PLAN
(WING 1- (WA&WB))
SCALE 1:100

GROUND FLOOR PLAN
WING 2-(WC)

15 CAR PARKING

PROPOSED 12.00M WIDE ROAD